


Budge St Development
Clark Construction
36A Budge Street

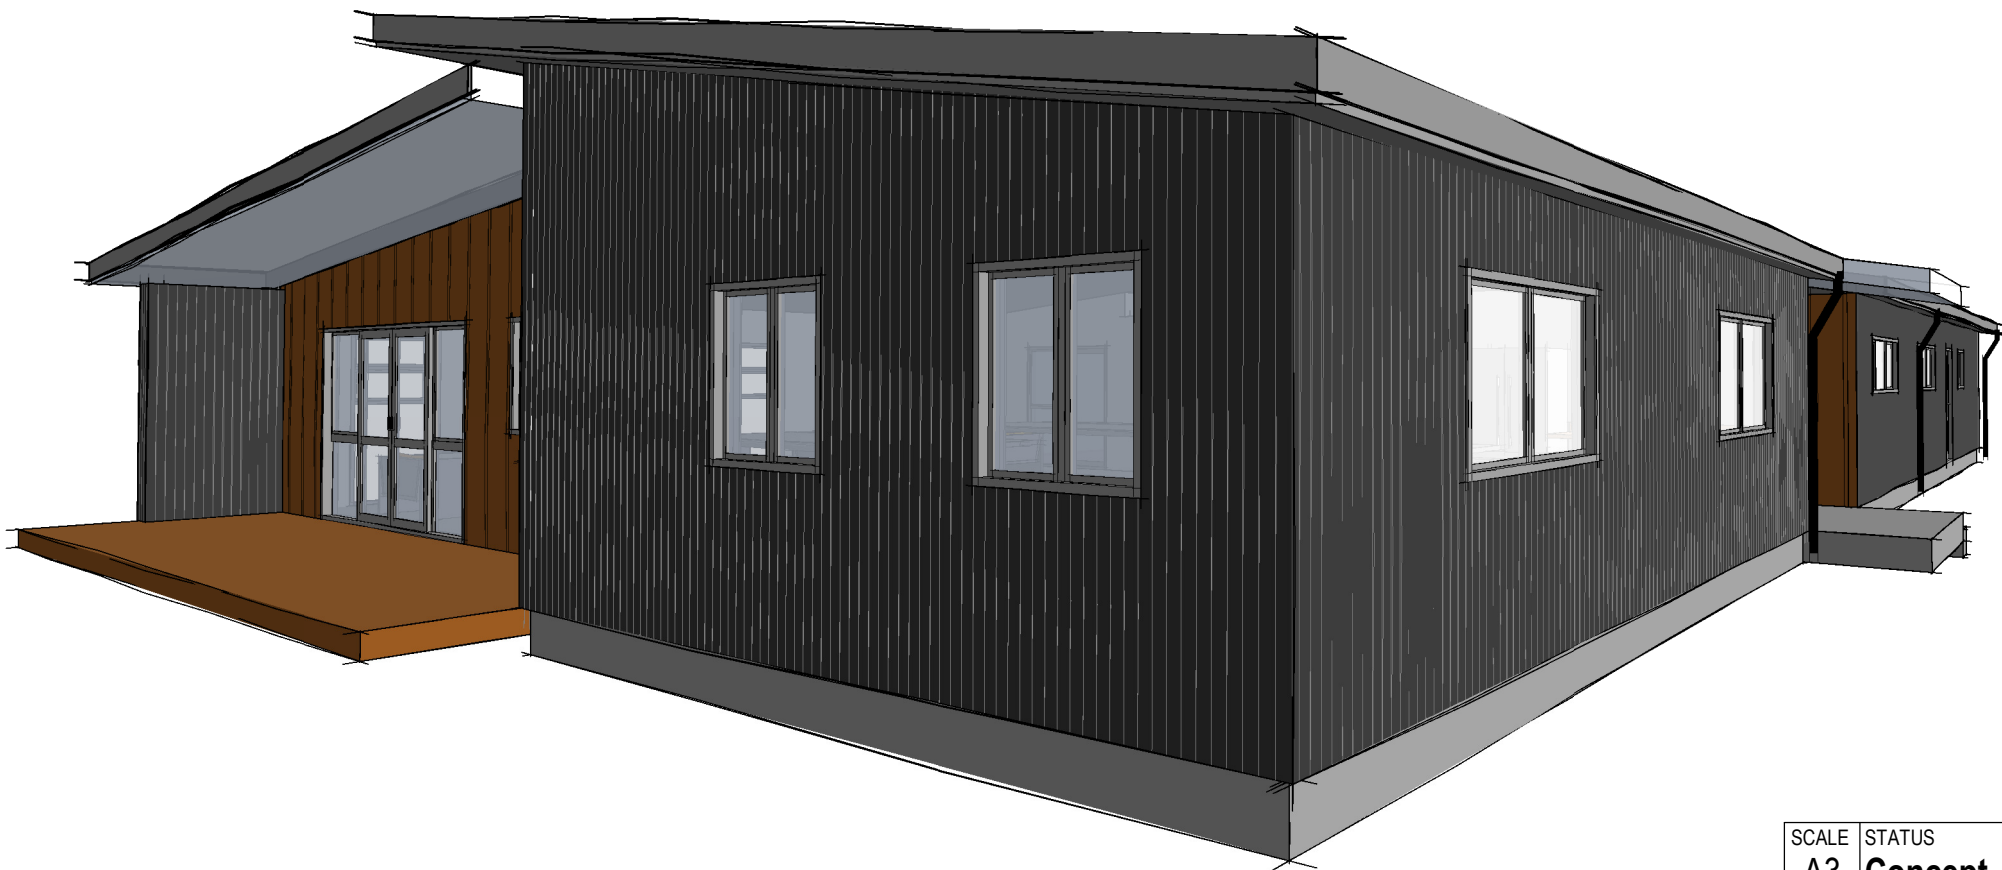

GENERAL NOTES

UNLESS OTHERWISE INDICATED, ALL DIMENSIONS ARE GIVEN IN MILLIMETERS. DO NOT SCALE OFF DRAWINGS.

The Design, information & technical detailing contained herein is copyright of Smart Alliances Ltd. Any adaption, distribution, or any form of reproduction of these works, in any part or in their entirety is prohibited.

PROJECT INFORMATION

Territorial Authority:

Reference Numbers
Resource Consent :
Project Information Memorandum:
Building Consent:

Legal Description:
Resource Management Plan:
Zone:


Topographic Class:
Earthquake Zone :
Exposure Zone :

Wind Region :
Wind Zone :
Snow Loading:

DRAWING REGISTER

DWG	Sheet Name	Revision	Date	Revision
A01	Floor plan	B	05/04/19	Revision B - fire design
A05	Elevations	B	05/04/19	Revision B - fire design
A11	Roof Plan	B	05/04/19	Revision B - fire design


- NOTES**
- Fire rated doors between suites to have closers with electro magnetic hold opens which are linked to the fire alarm activation so that the door is released upon activation of alarm.
 - Type 5 fire alarm system smoke detectors throughout
 - Fire walls (as indicated in red) full height to underside of roof
 - External fire rating wall requirement yet to be determined
 - House divided into fire sleeping suites

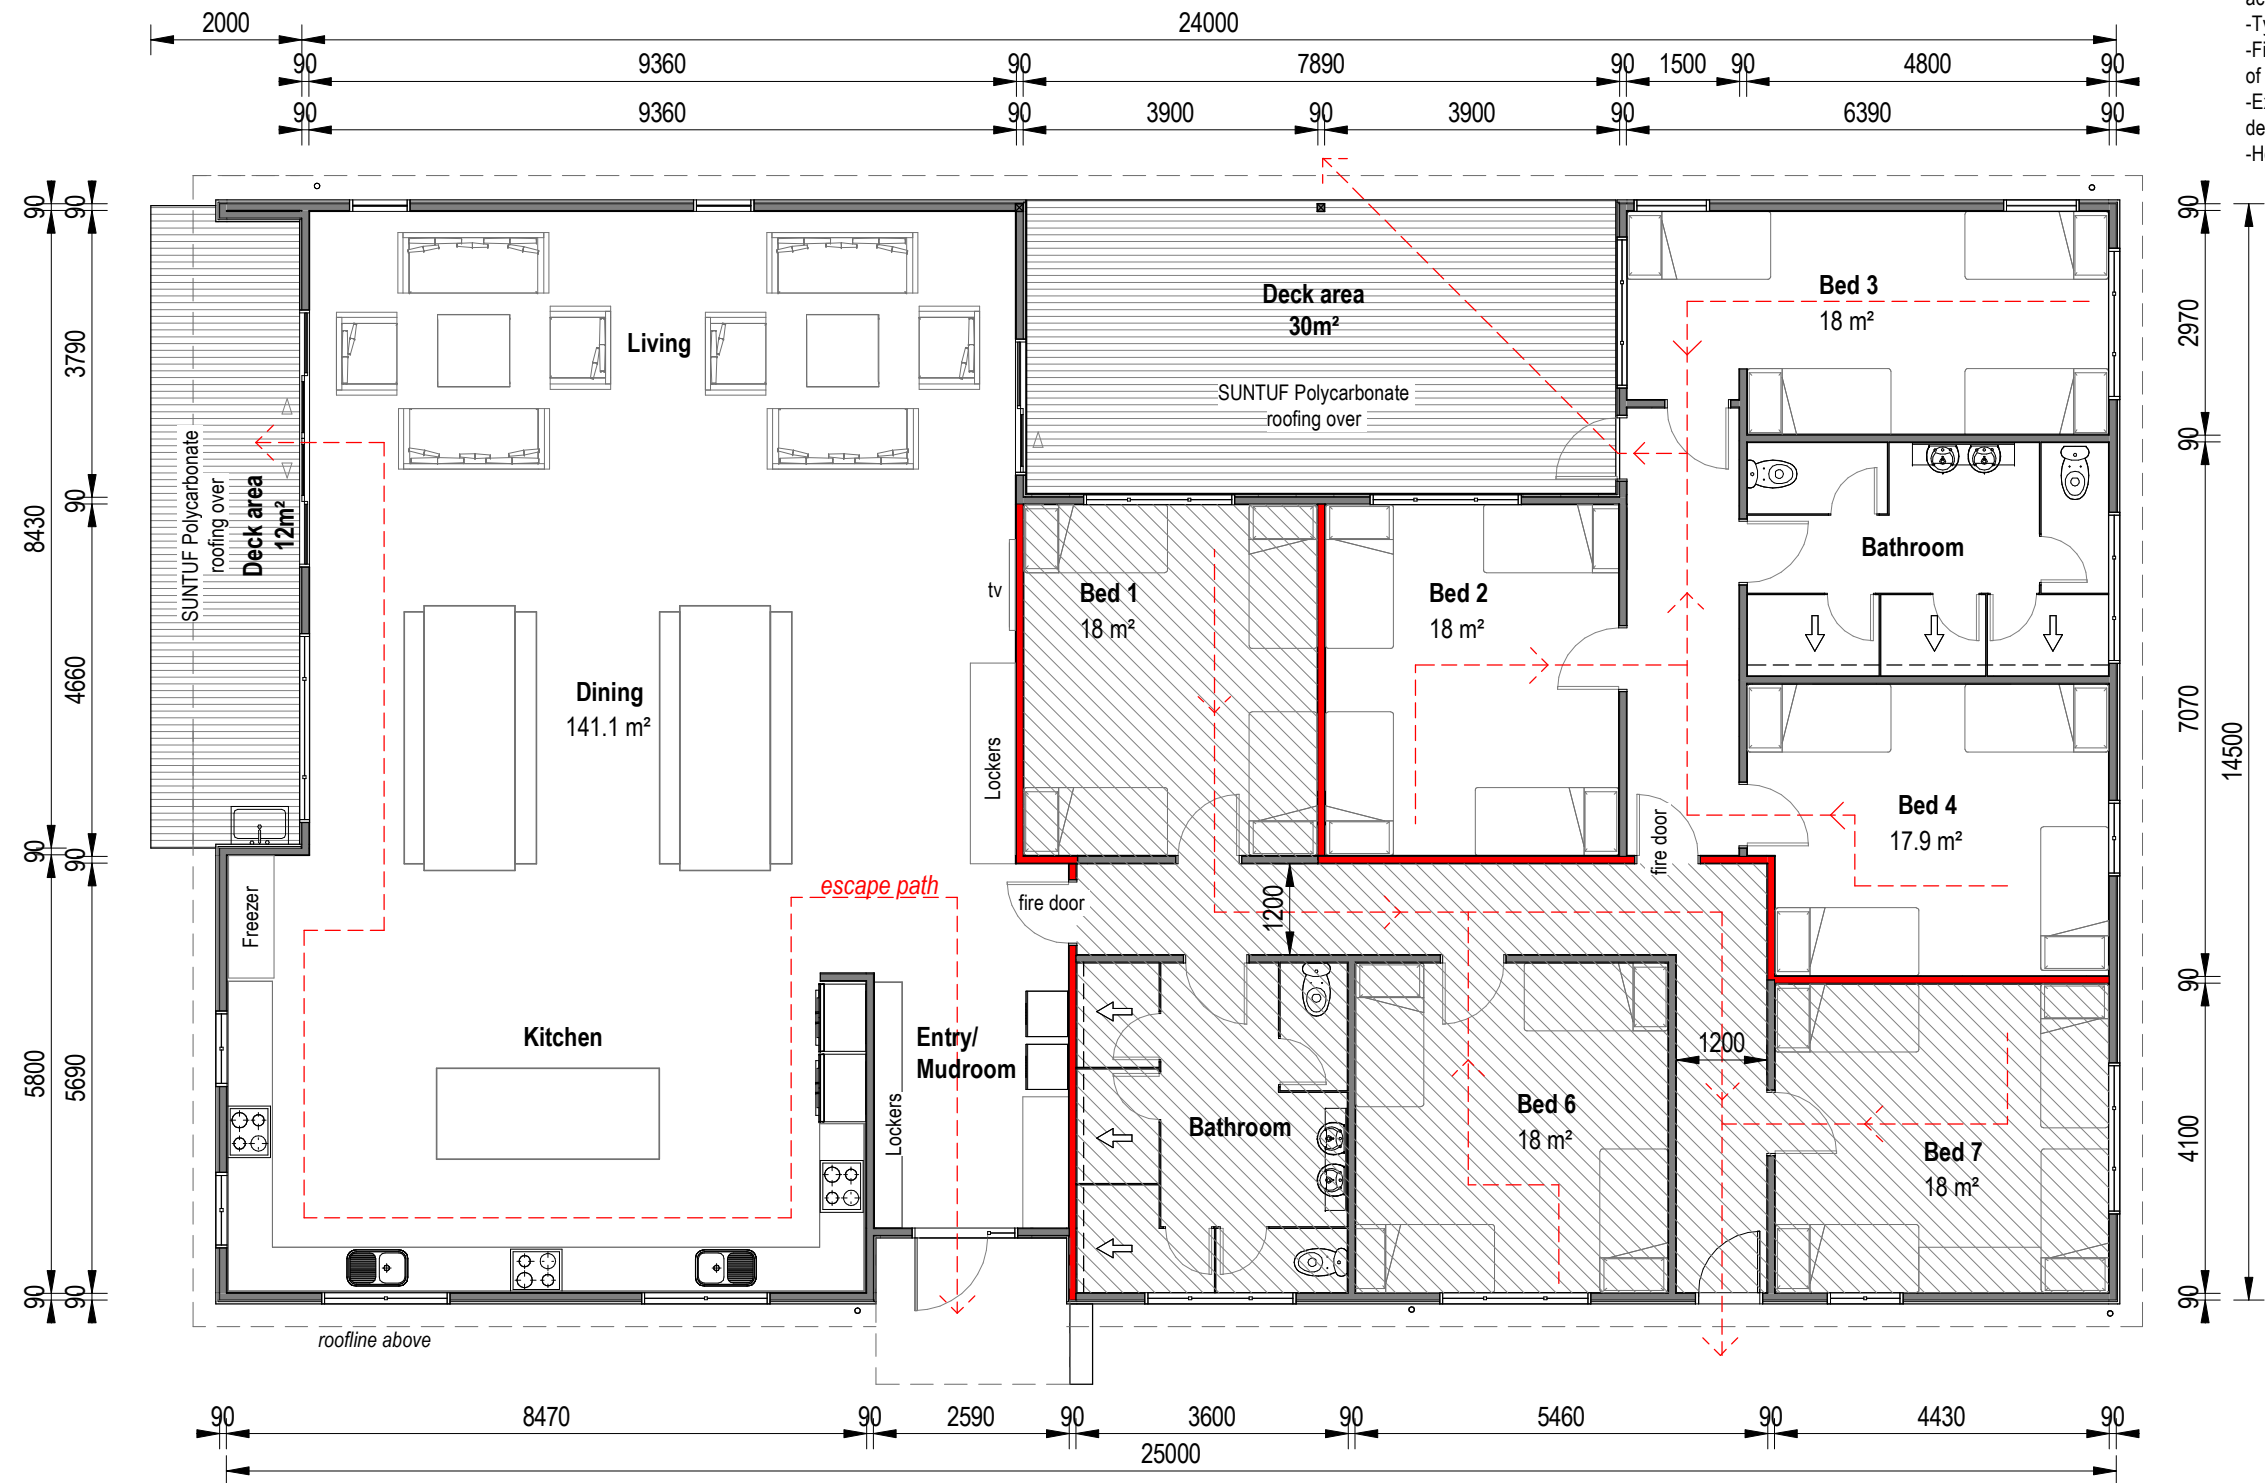


1
A01
Floor plan
Scale 1 : 100

Do not scale from this drawing.
Verify all dimensions on site prior to construction.


REV	DATE	DESCRIPTION	 ENGINEERING / RESOURCE MANAGEMENT / ARCHITECTS LTD 1st Floor - River View House - 10 High Street - Blenheim - New Zealand T: 03 579 6211 F: 03 579 6233 PO Box 546 - Blenheim - 7240 E: info@smartalliances.co.nz Website: www.smartalliances.co.nz	PROJECT Budge St Development 36A Budge Street CLIENT Clark Construction	DRAWING Floor plan ORIGIN DATE 05/03/19	STATUS Concept	
A	12/03/19	Revision A				DESIGNED SH	SCALE (A3) 1 : 100
B	05/04/19	Revision B - fire design				DRAWN SH APPROVED	REVISION DATE 05/04/19 DWG NO. 7092-A01 REVISION B

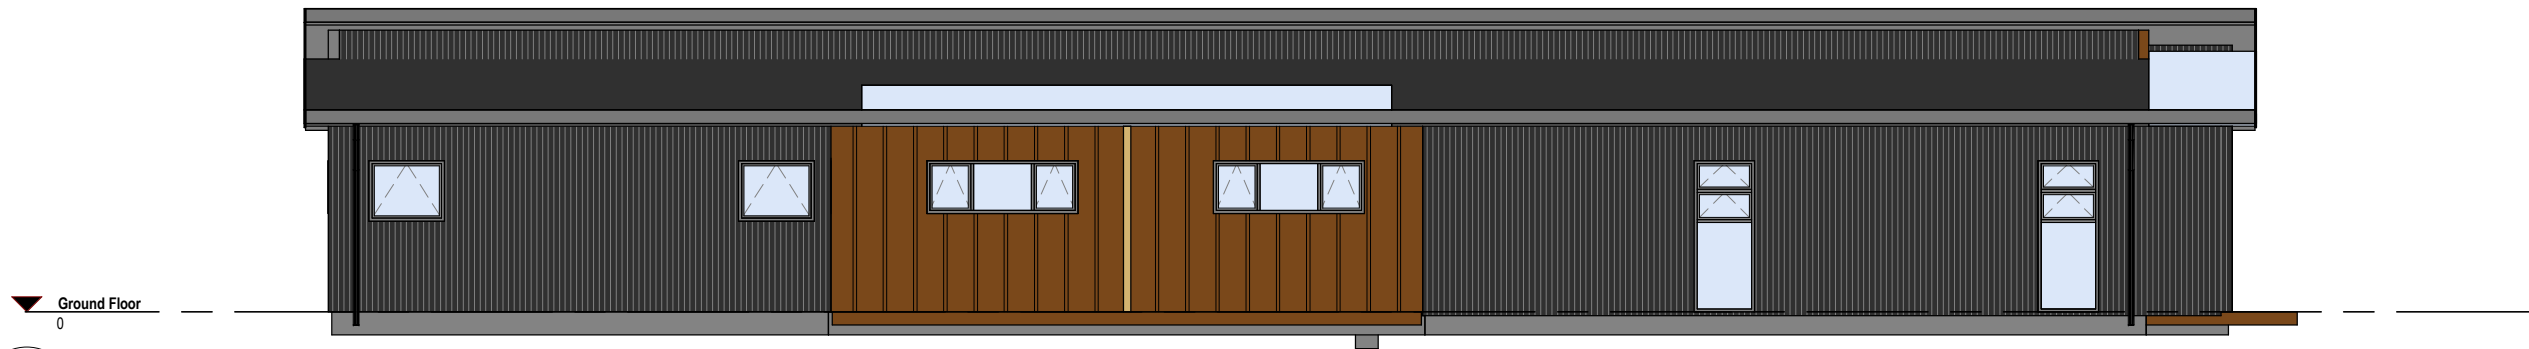

1 North Elevation
A05 Scale 1 : 100

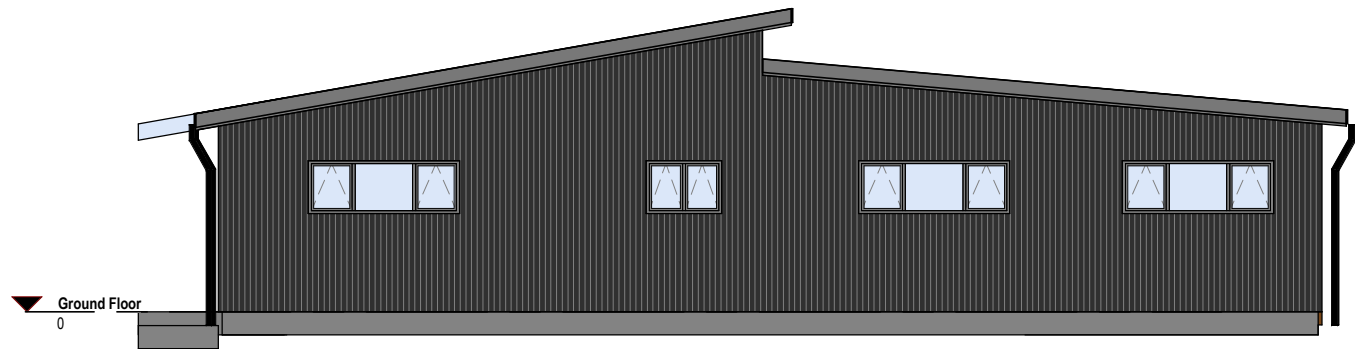

2 East Elevation
A05 Scale 1 : 100

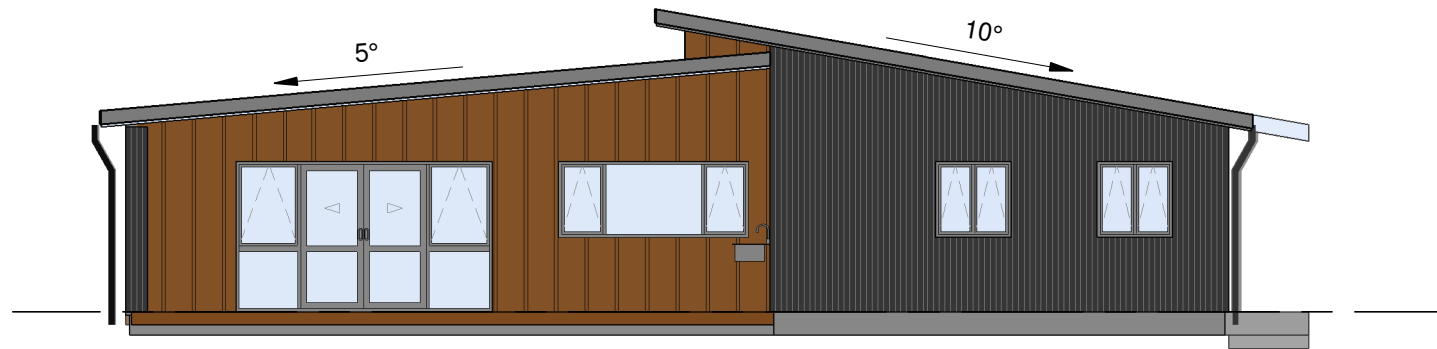

3 West Elevation
A05 Scale 1 : 100



4 South Elevation
A05 Scale 1 : 100

Do not scale from this drawing.
Verify all dimensions on site prior to construction.


REV	DATE	DESCRIPTION
B	05/04/19	Revision B - fire design

 **smartalliances**
ENGINEERING / RESOURCE MANAGEMENT / ARCHITECTS LTD
1st Floor - River View House - 10 High Street - Blenheim - New Zealand
T: 03 579 6211 F: 03 579 6233 PO Box 546 - Blenheim - 7240
E: info@smartalliances.co.nz Website: www.smartalliances.co.nz

PROJECT
Budge St Development
36A Budge Street
CLIENT
Clark Construction

DRAWING
Elevations
ORIGIN DATE
05/03/19

STATUS		
Concept		
DESIGNED	SCALE (A3)	
Designer	1 : 100	
DRAWN	REVISION DATE	
Author	05/04/19	
APPROVED	DWG NO.	REVISION
Approver	7092-A05	B

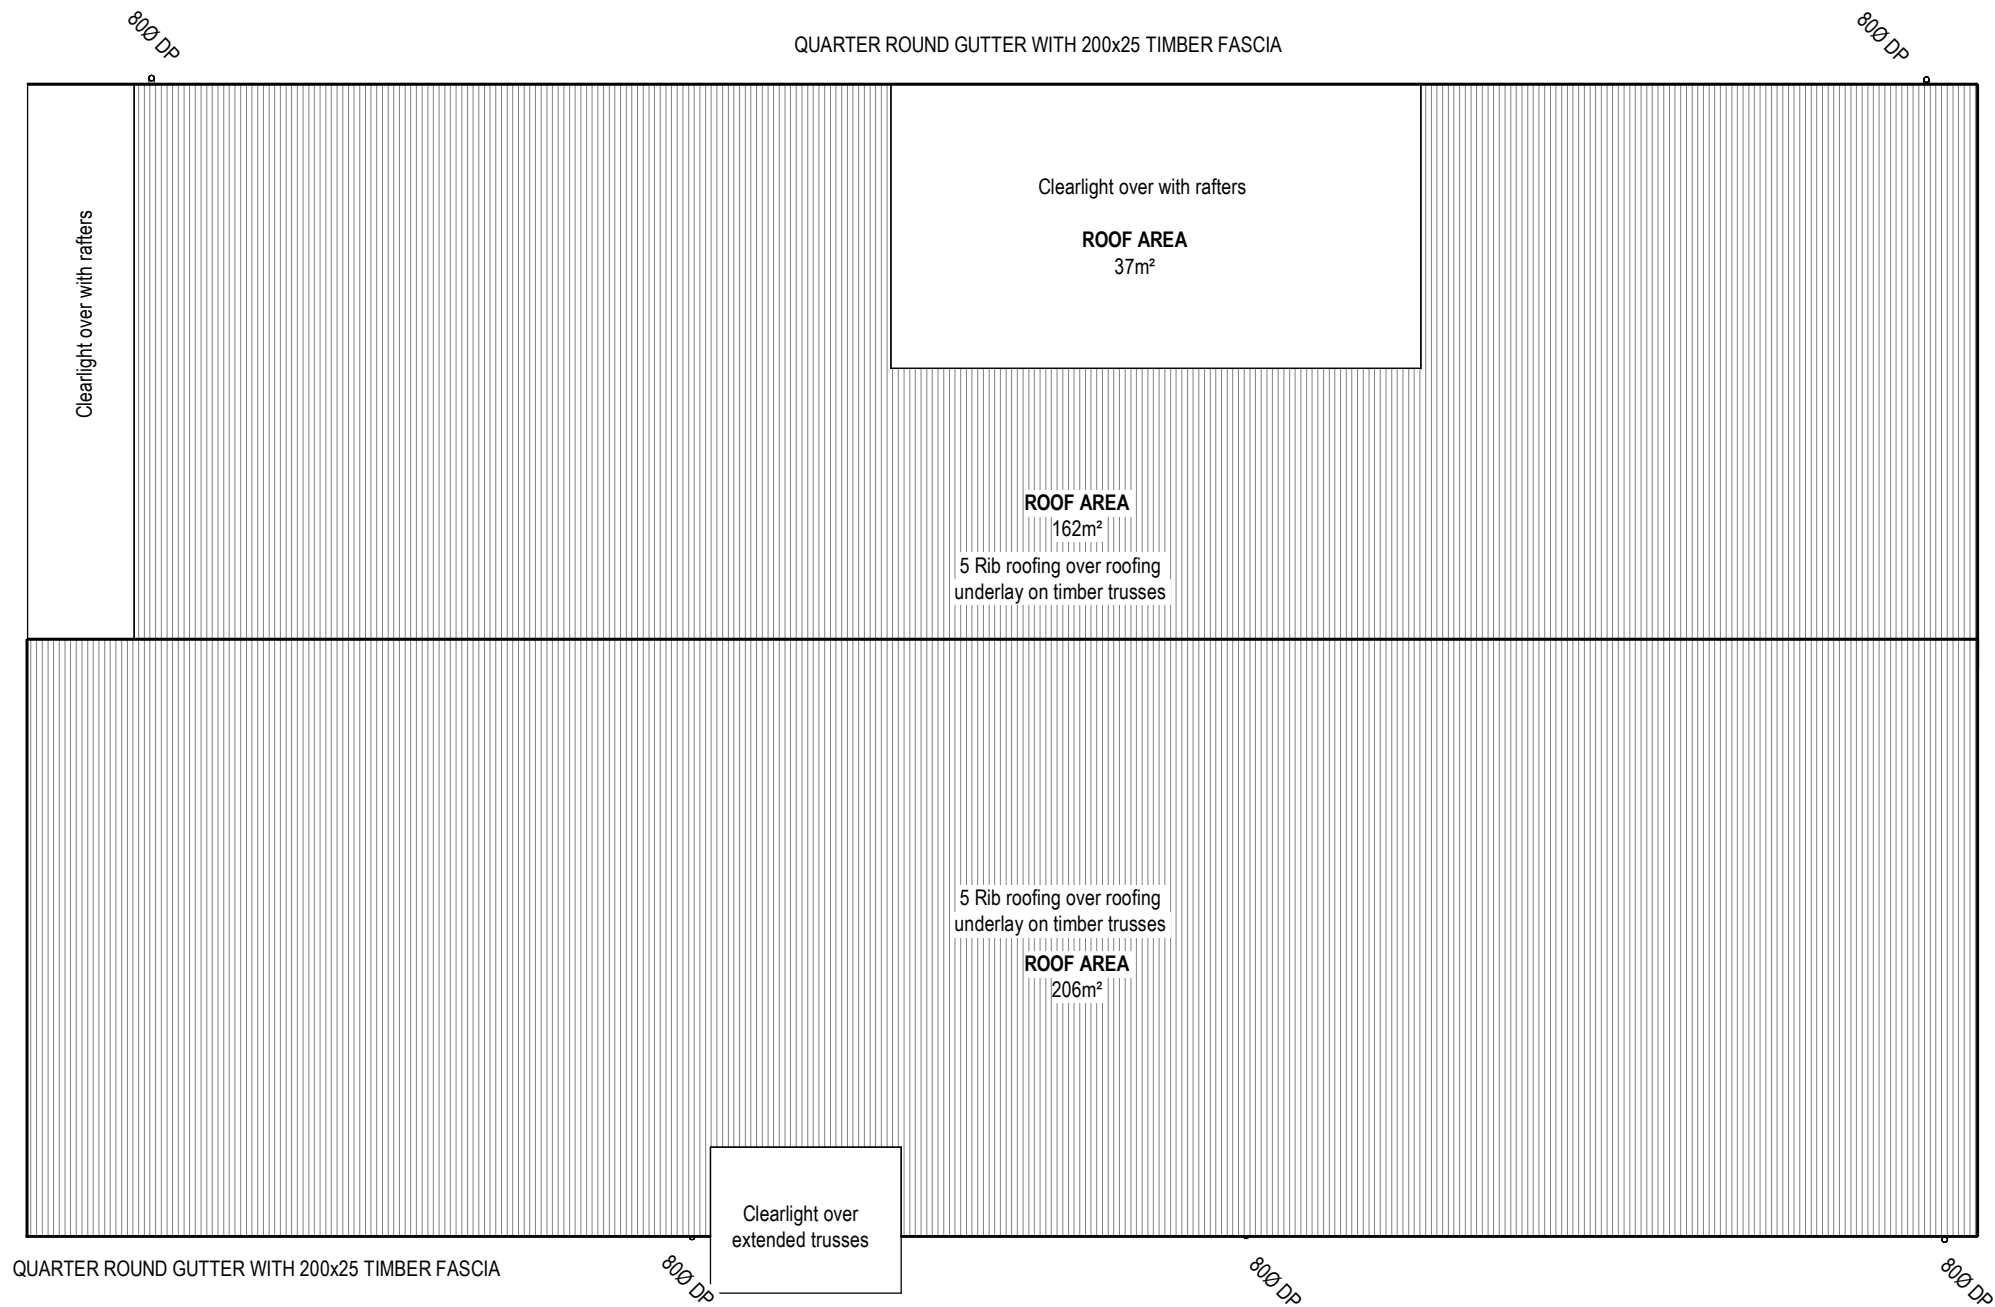

1
A11

Roof Plan
Scale 1 : 100

Do not scale from this drawing.
Verify all dimensions on site prior to construction.

REV	DATE	DESCRIPTION	 smartalliances ENGINEERING / RESOURCE MANAGEMENT / ARCHITECTS LTD 1st Floor · River View House · 10 High Street · Blenheim · New Zealand T: 03 579 6211 F: 03 579 6233 PO Box 546 · Blenheim · 7240 E: info@smartalliances.co.nz Website: www.smartalliances.co.nz	PROJECT	DRAWING	STATUS	
B	05/04/19	Revision B - fire design		Budge St Development 36A Budge Street	Roof Plan	Concept	
				CLIENT	ORIGIN DATE	DESIGNED Designer	SCALE (A3) 1 : 100
				Clark Construction	05/03/19	DRAWN Author	REVISION DATE 05/04/19
					APPROVED Approver	DWG NO. 7092-A11	REVISION B